


4.1 계측기 설치 및 공사현황

계측기설치 위치도

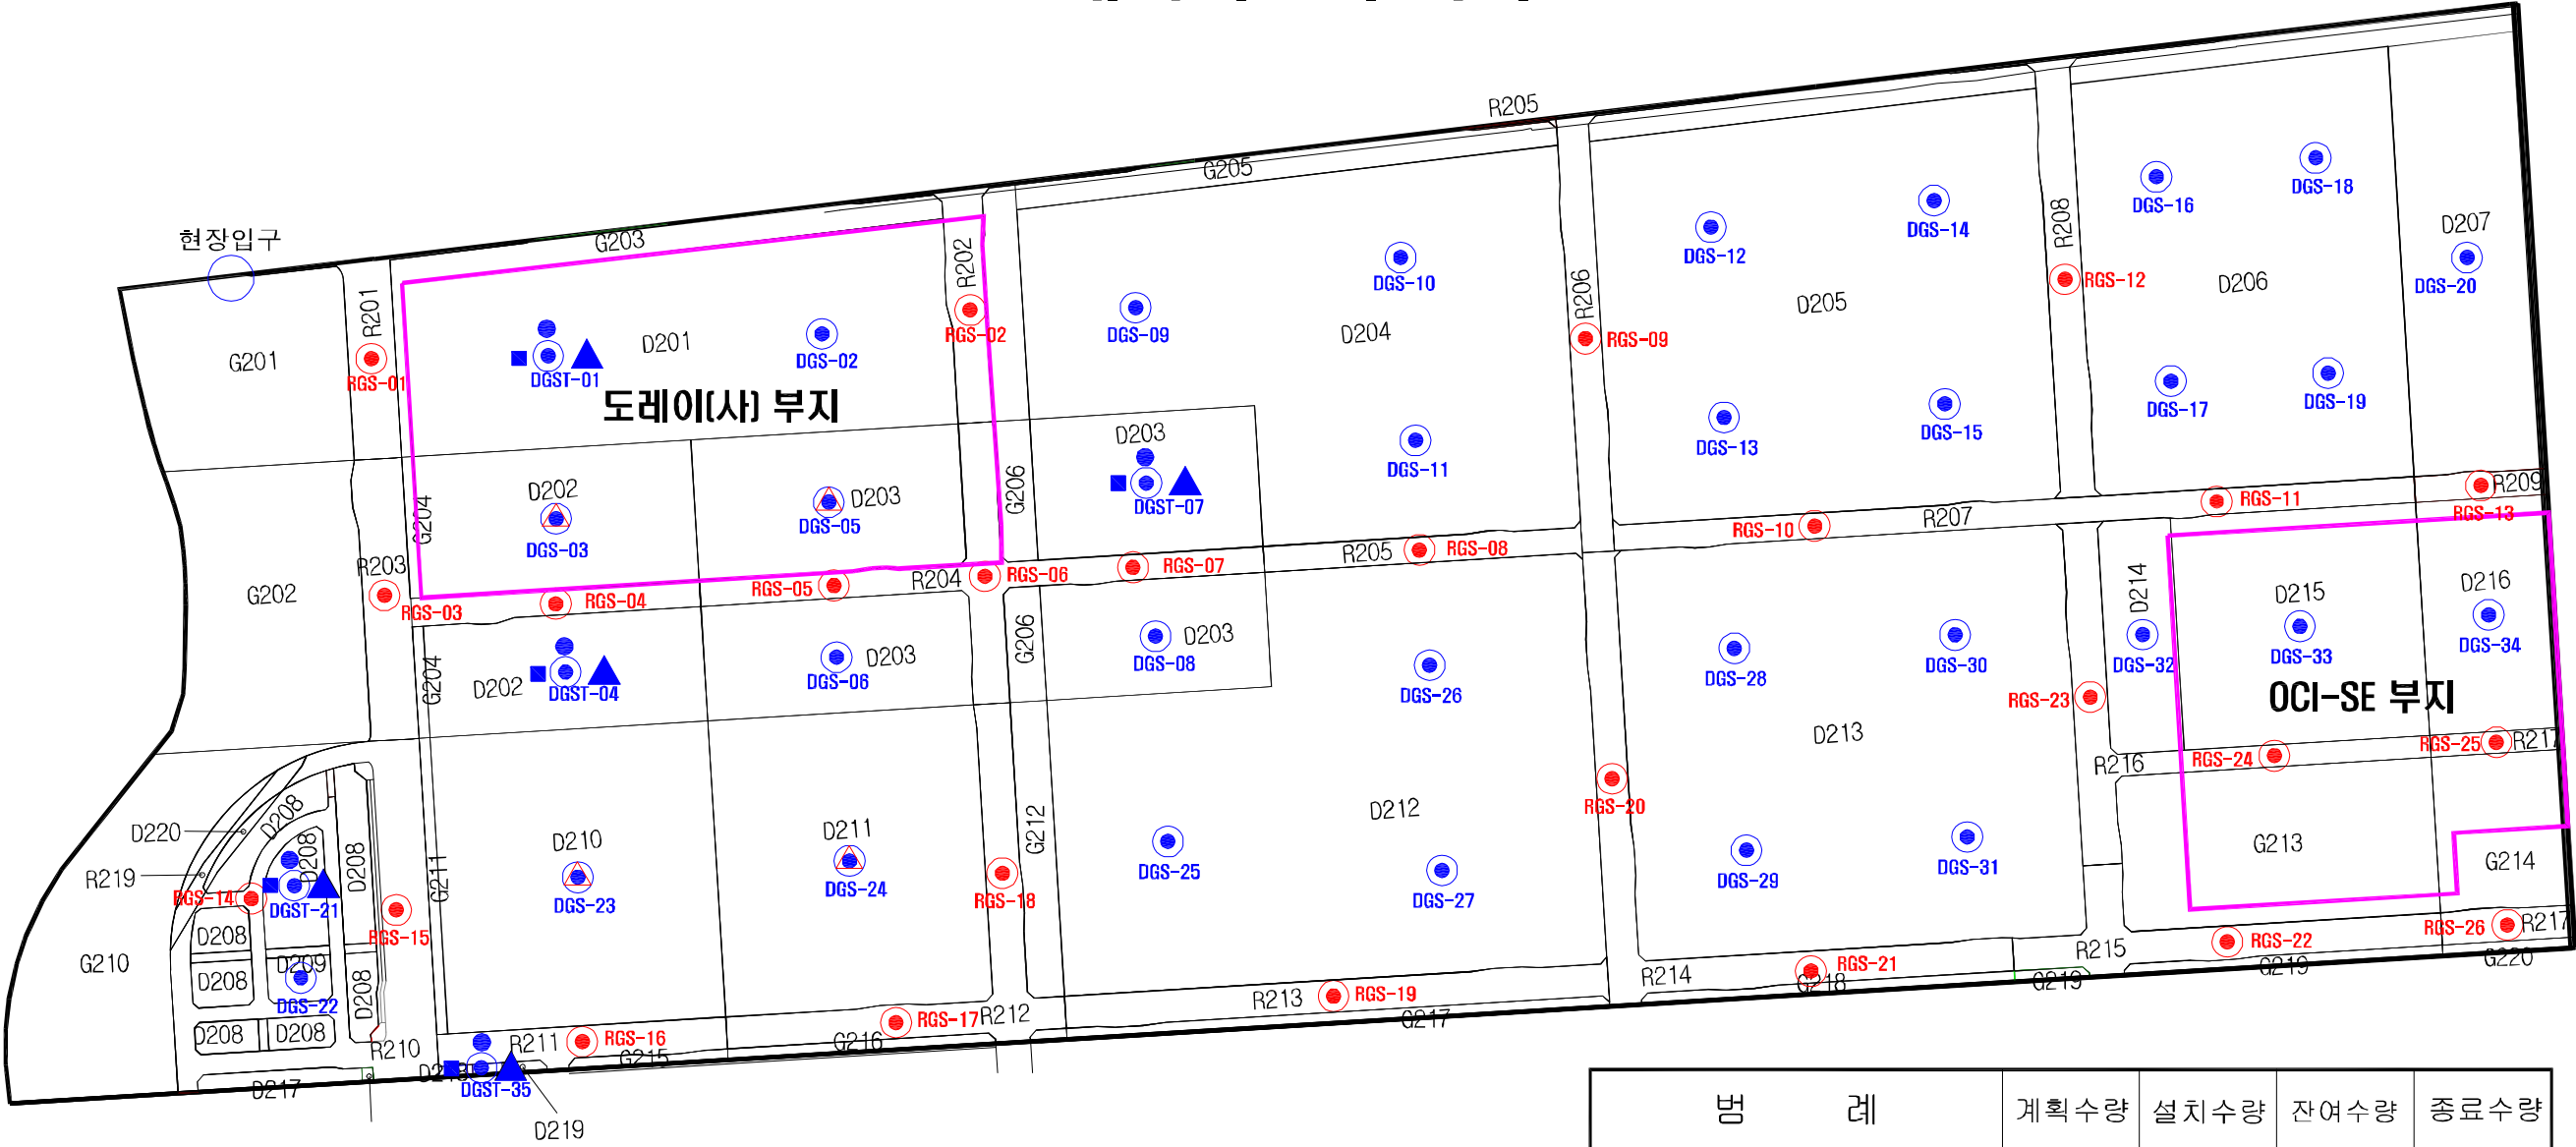


△ : 시공사 설치 계측기

범 례			계획수량	설치수량	잔여수량	종료수량
도 로	●	지표면침하판	26	26	0	2
단 지	◎	지표면침하판	35	35	0	2
	●	간극수압계	5	5	0	0
	■	지하수위계	5	5	0	0
	▲	층별 침하계	5	5	0	0

<그림 4.1> 계측기 설치 위치도


4.2 매립 현황도

매 립 현 황 도

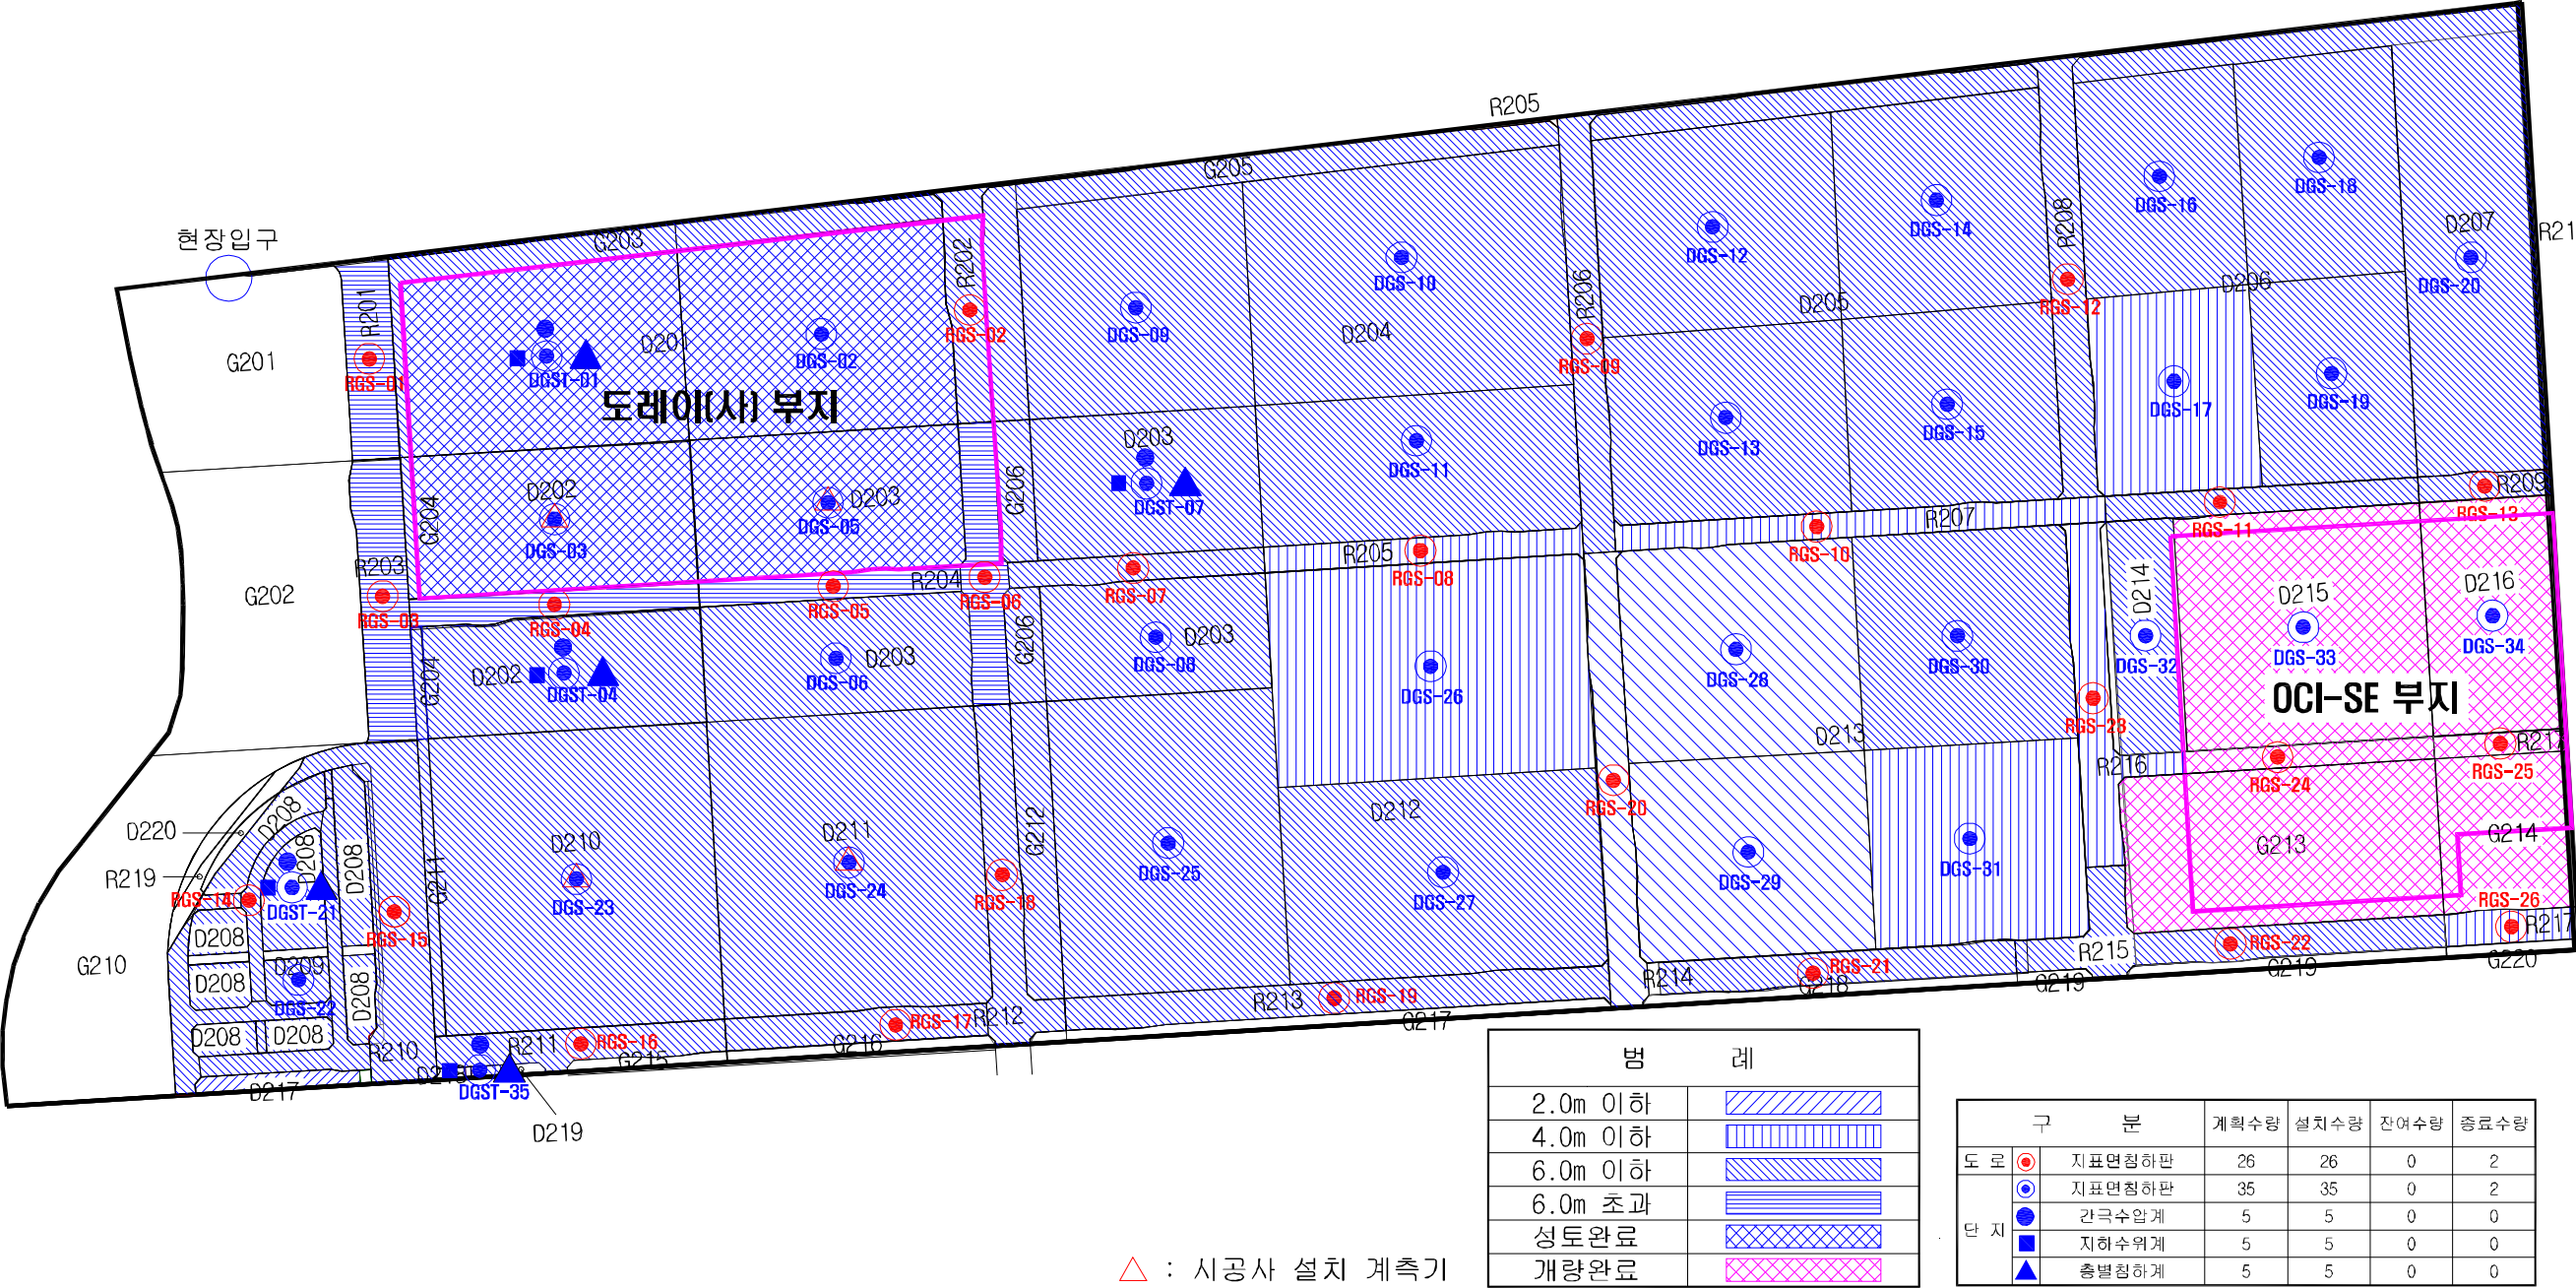


<그림 4.2> 매립 현황도

6.4 계측결과

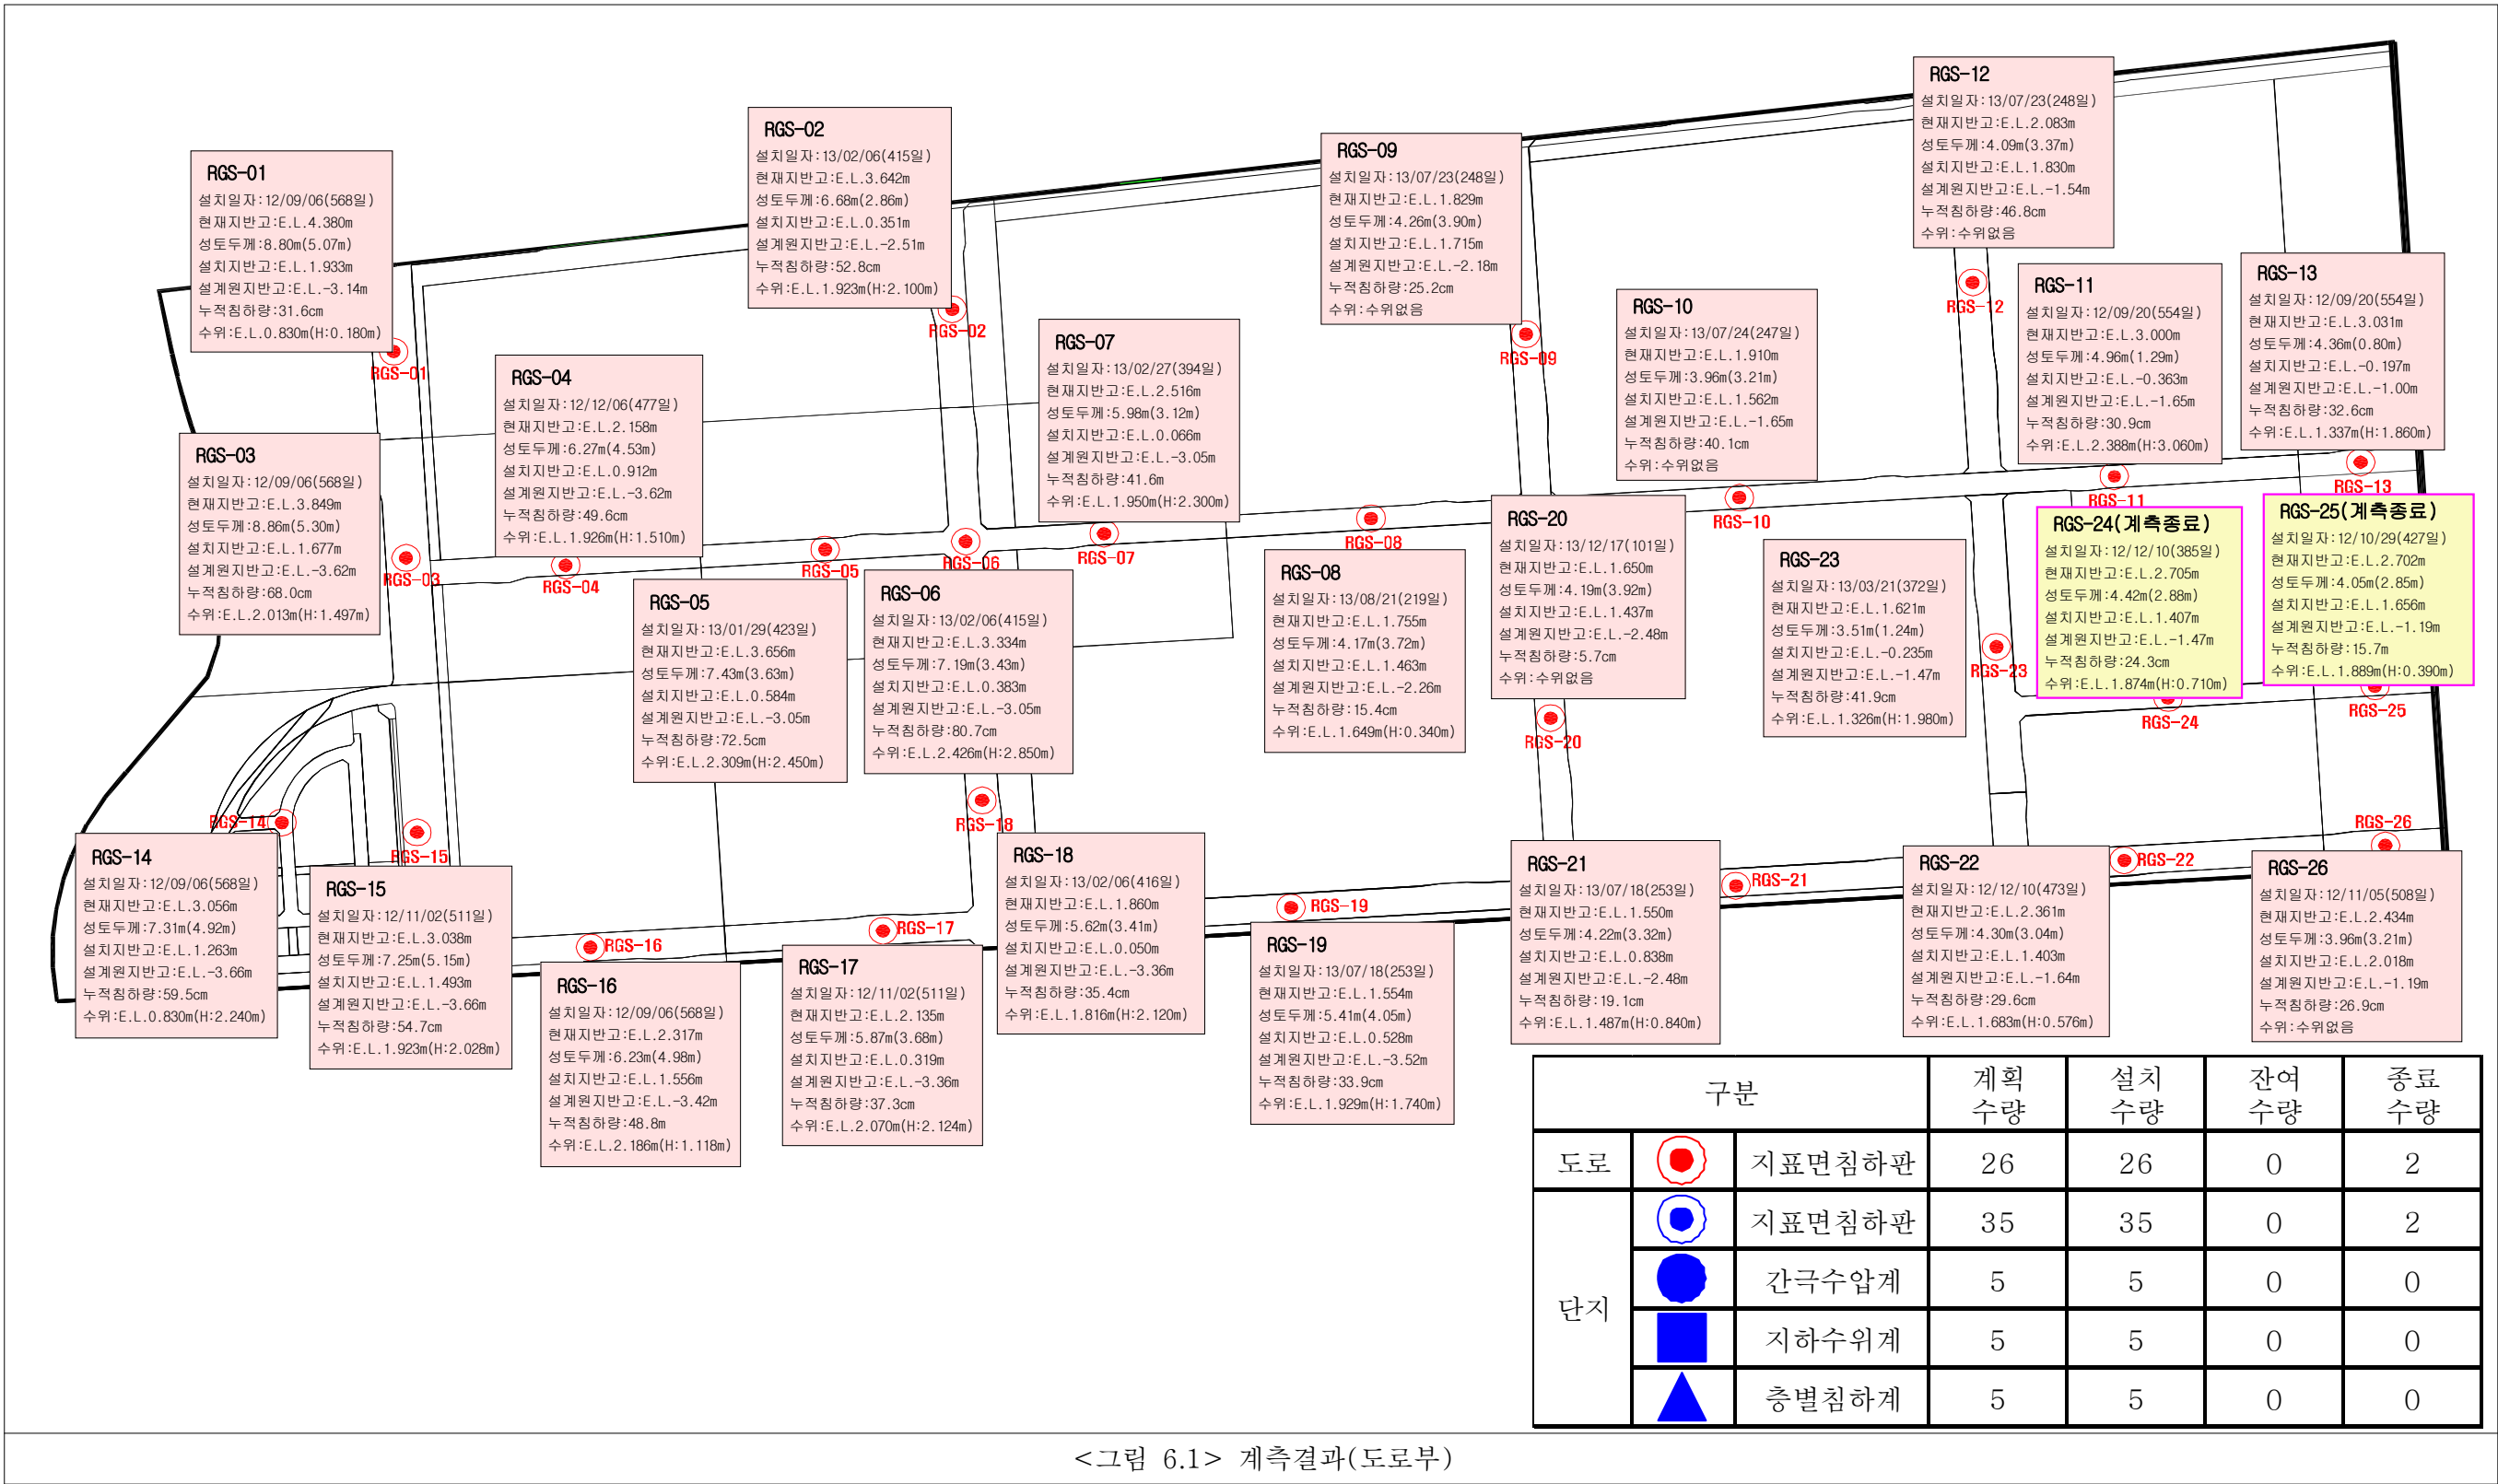

※성토두께 및 수위높이는 지표면침하판 기준임.

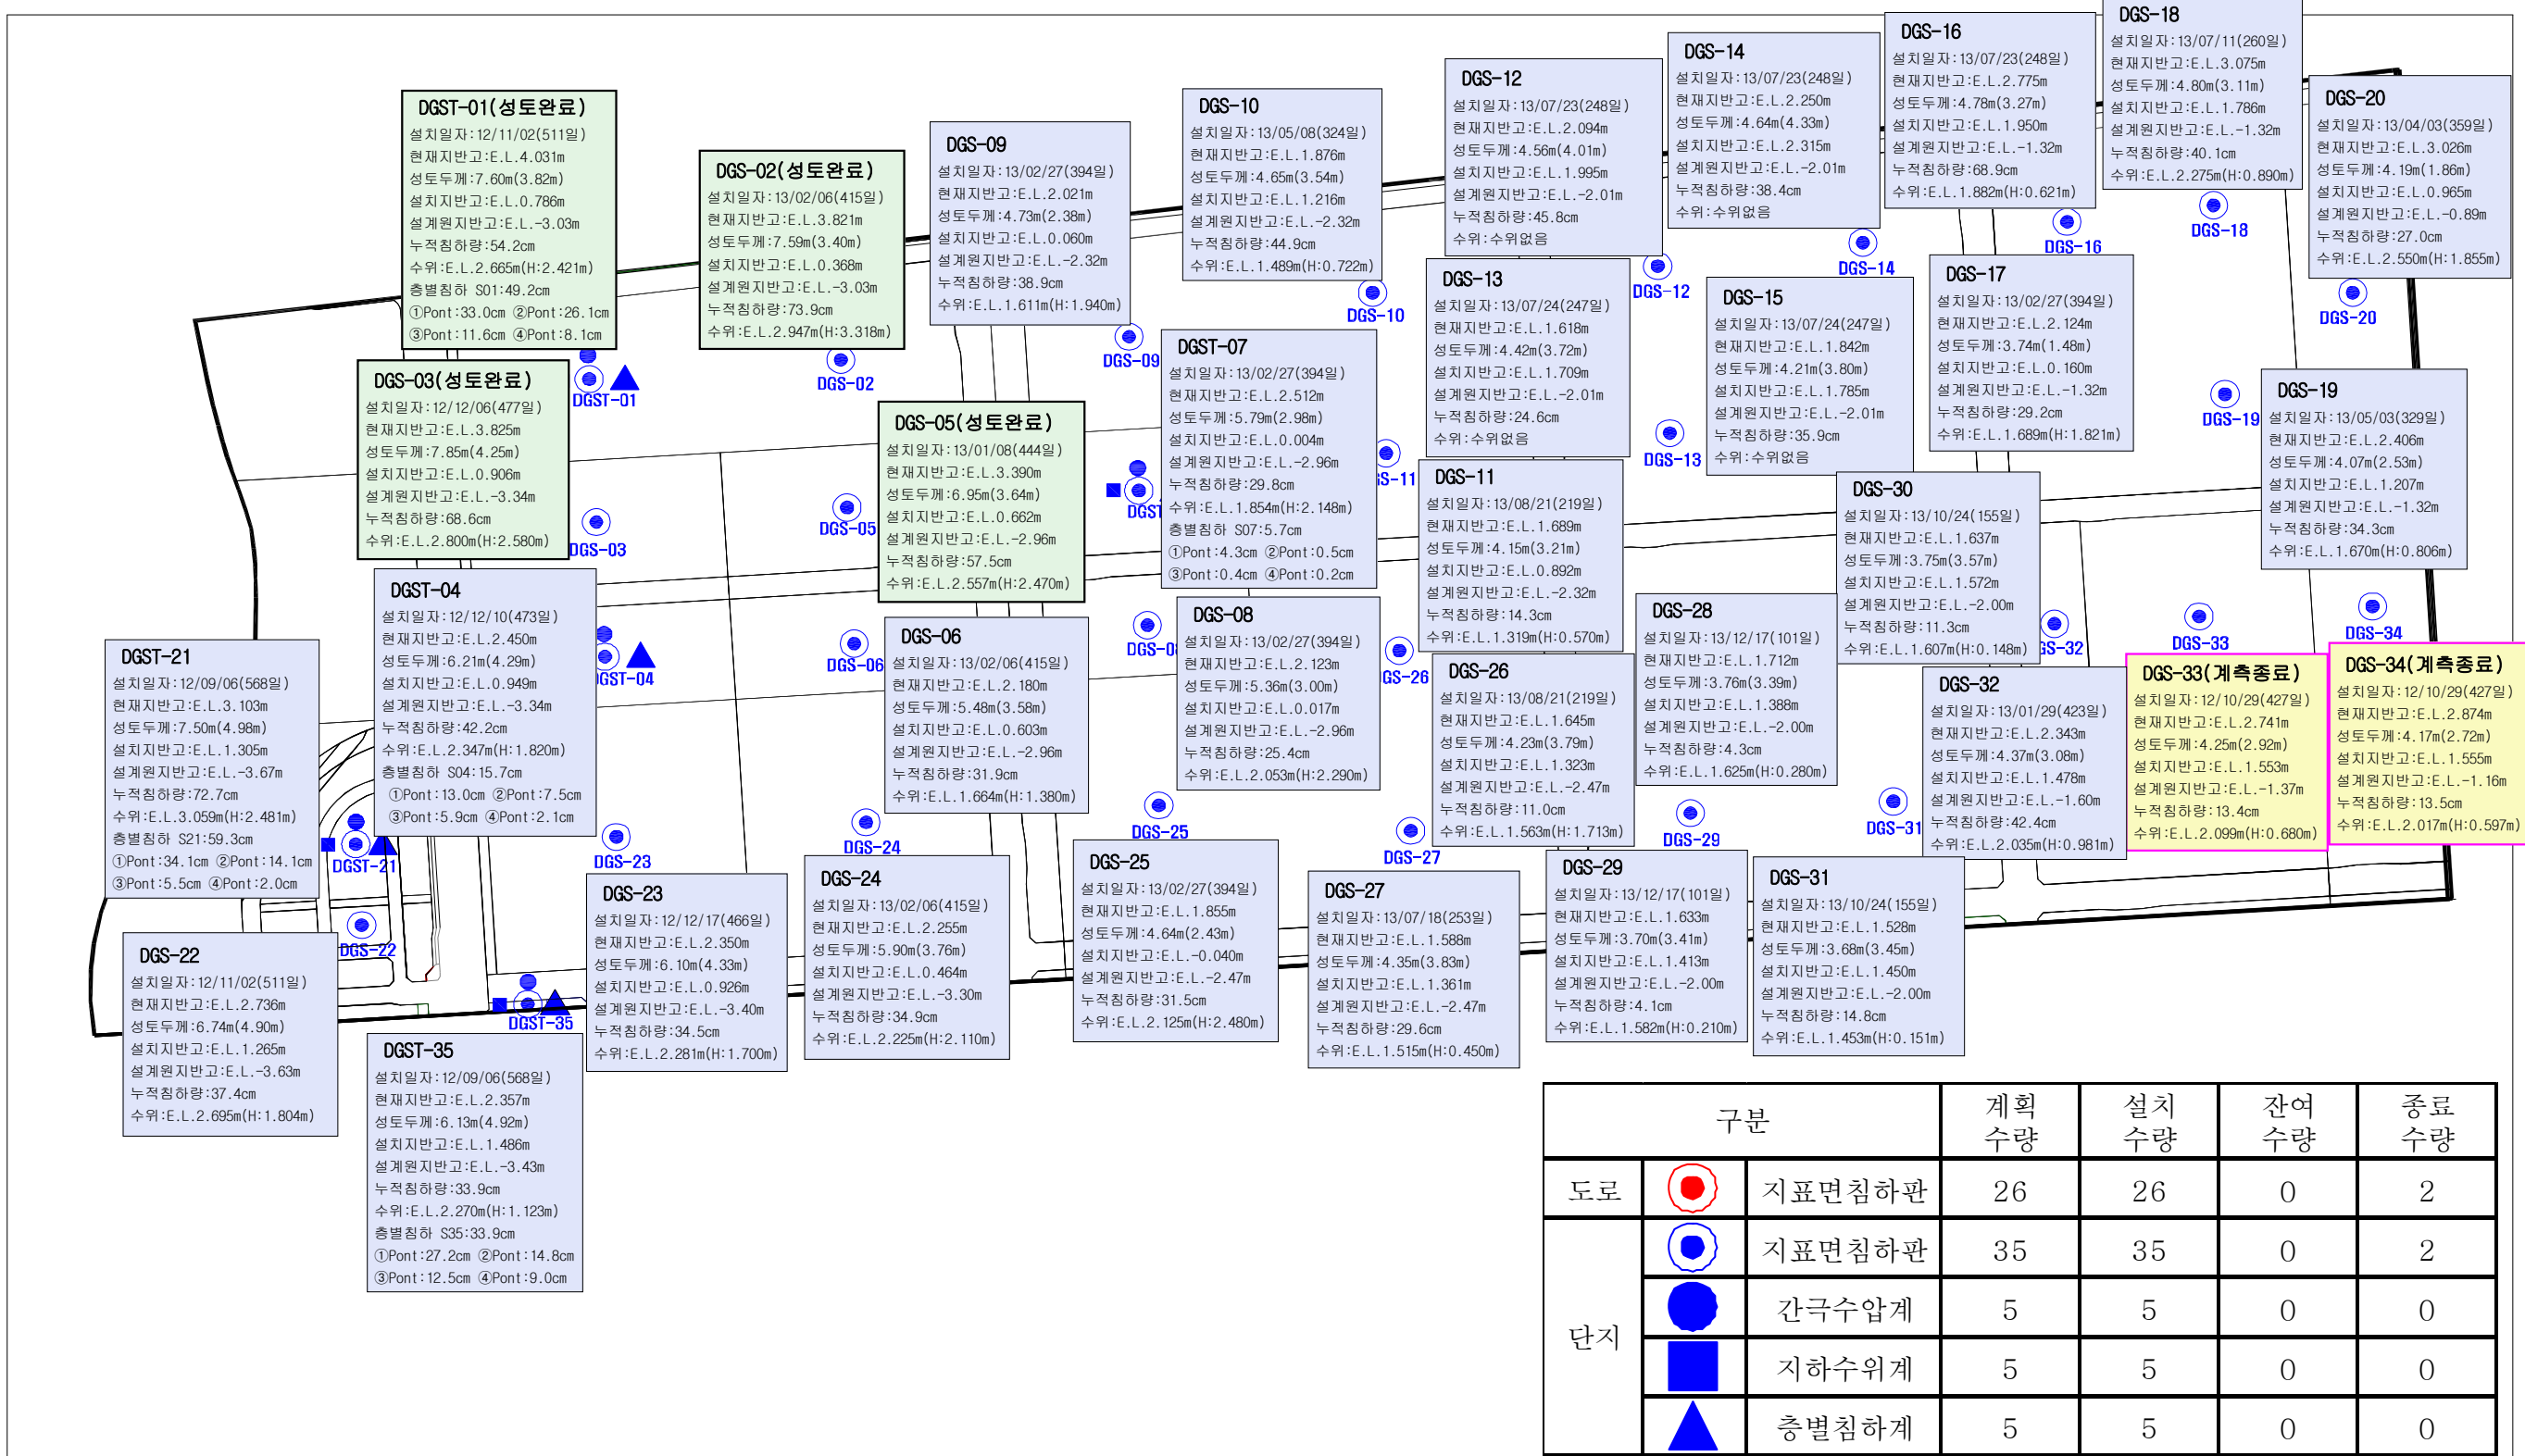

<그림 6.2> 계측결과(단지부)

※성토두께 및 수위높이는 지표면침하판 기준임.