



토공 계획계획도


① 연약지반 및 성토

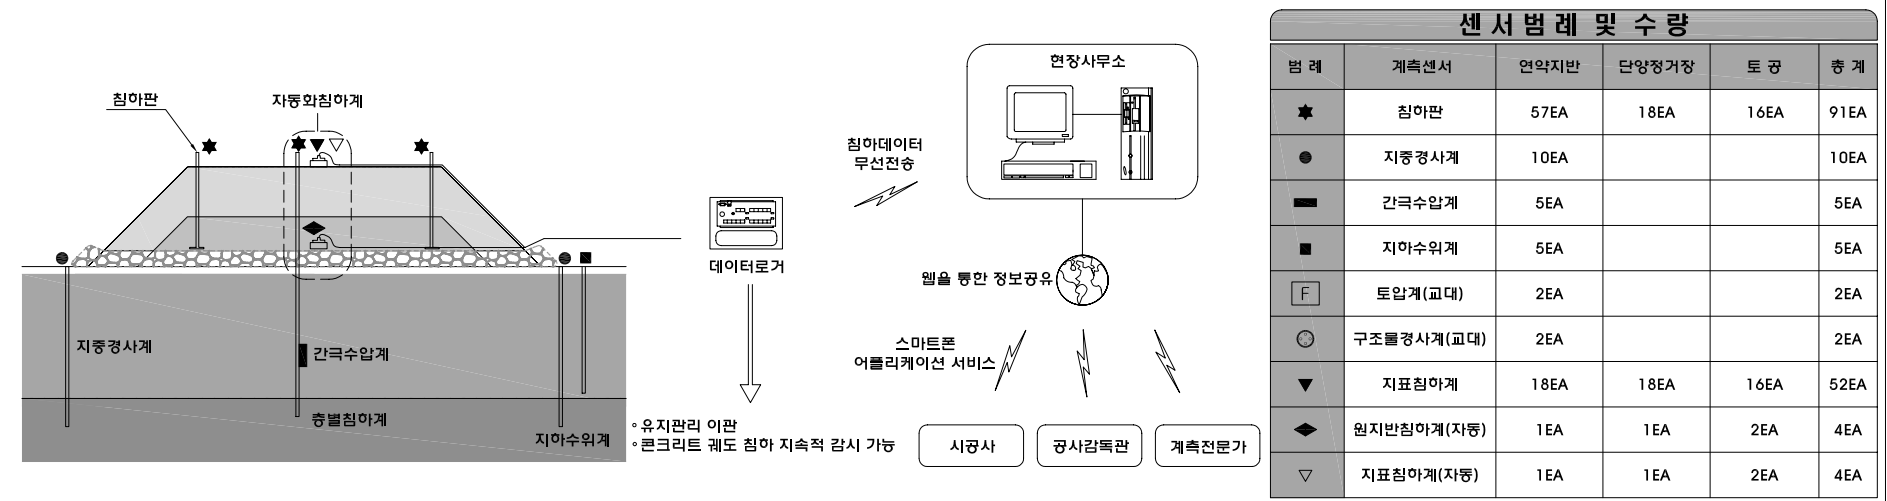


② 정거장 가시설

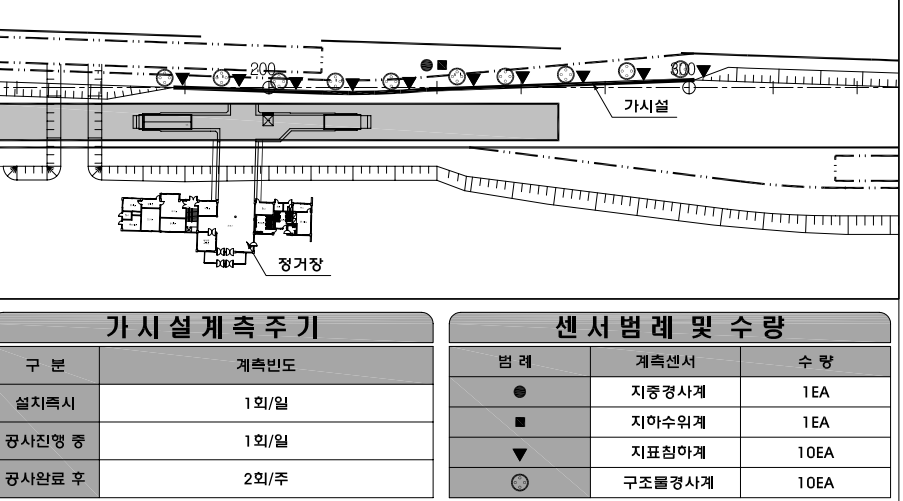

중단면도

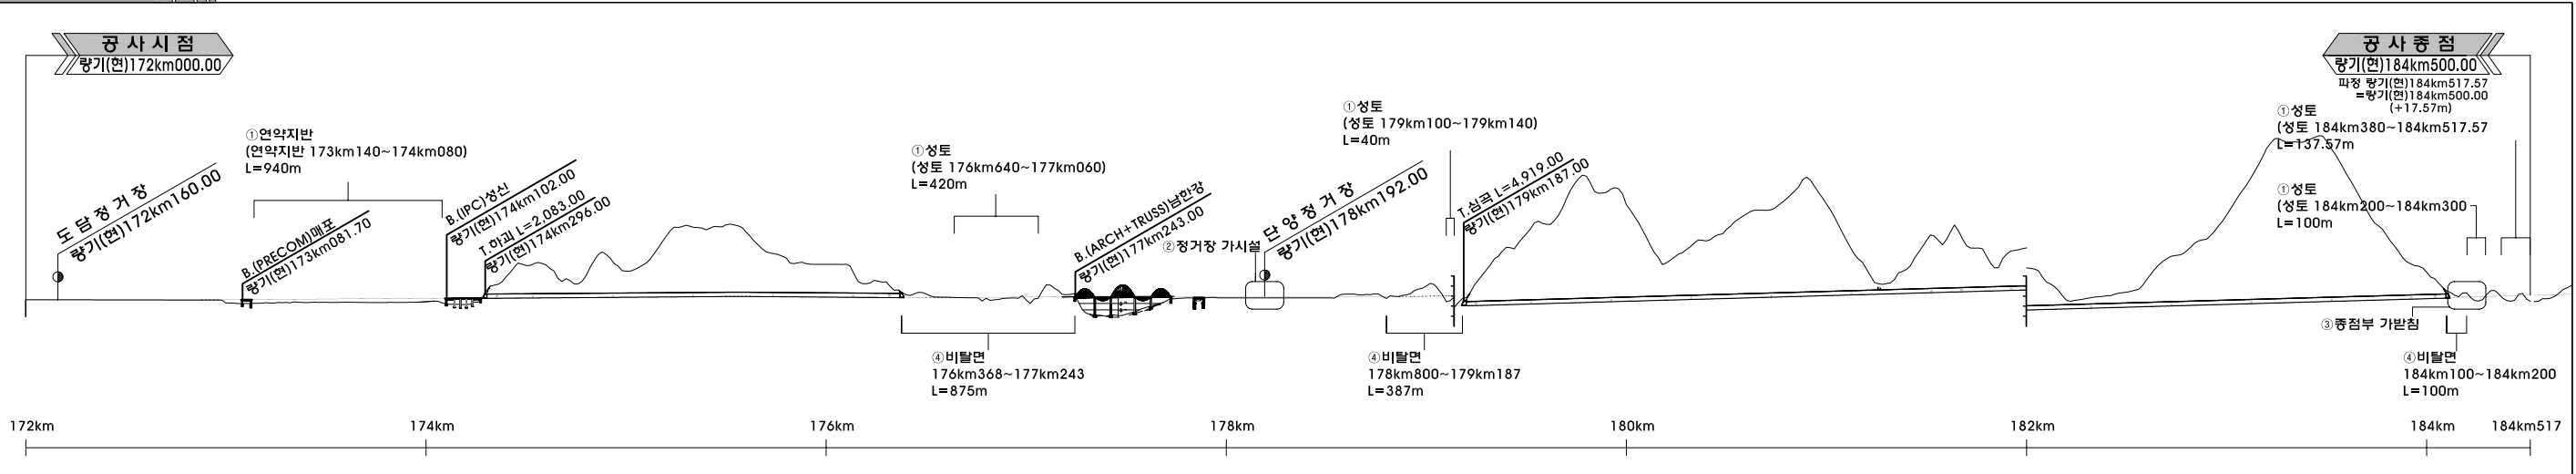

③ 종점부 가설교량

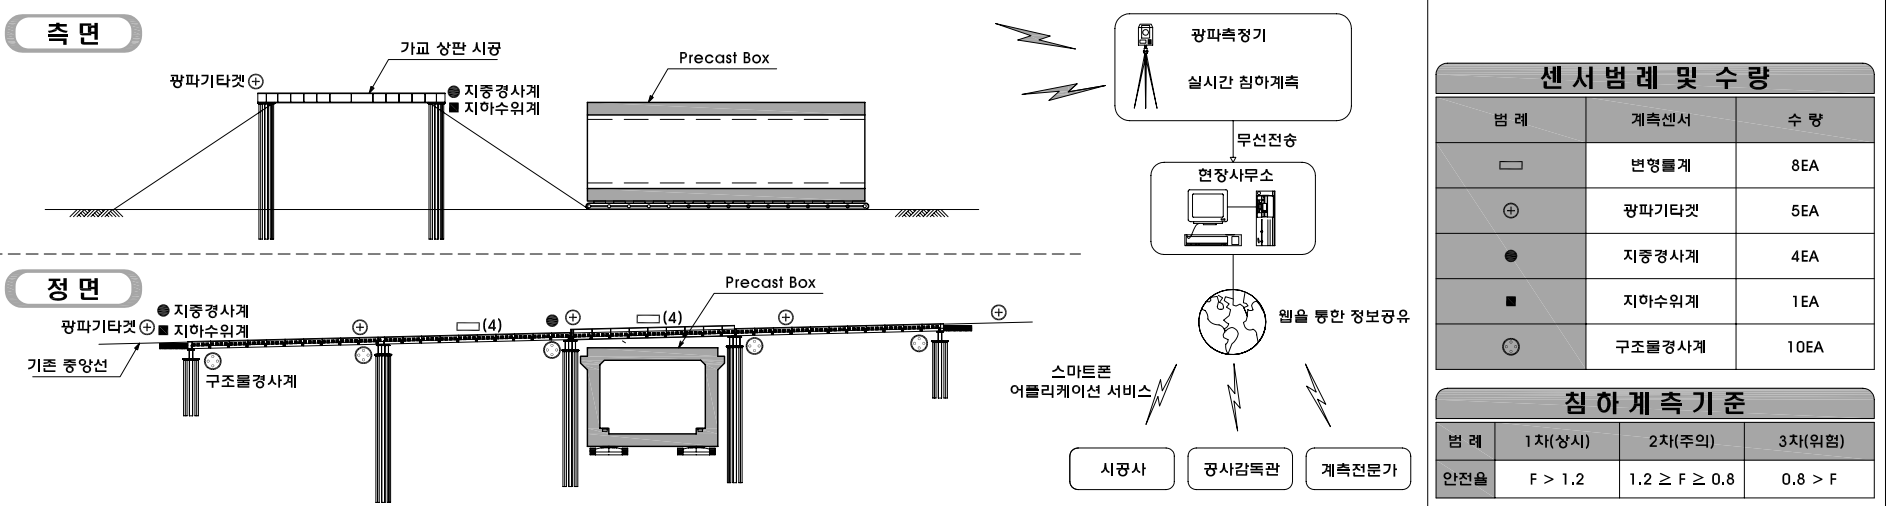

④ 비탈면

